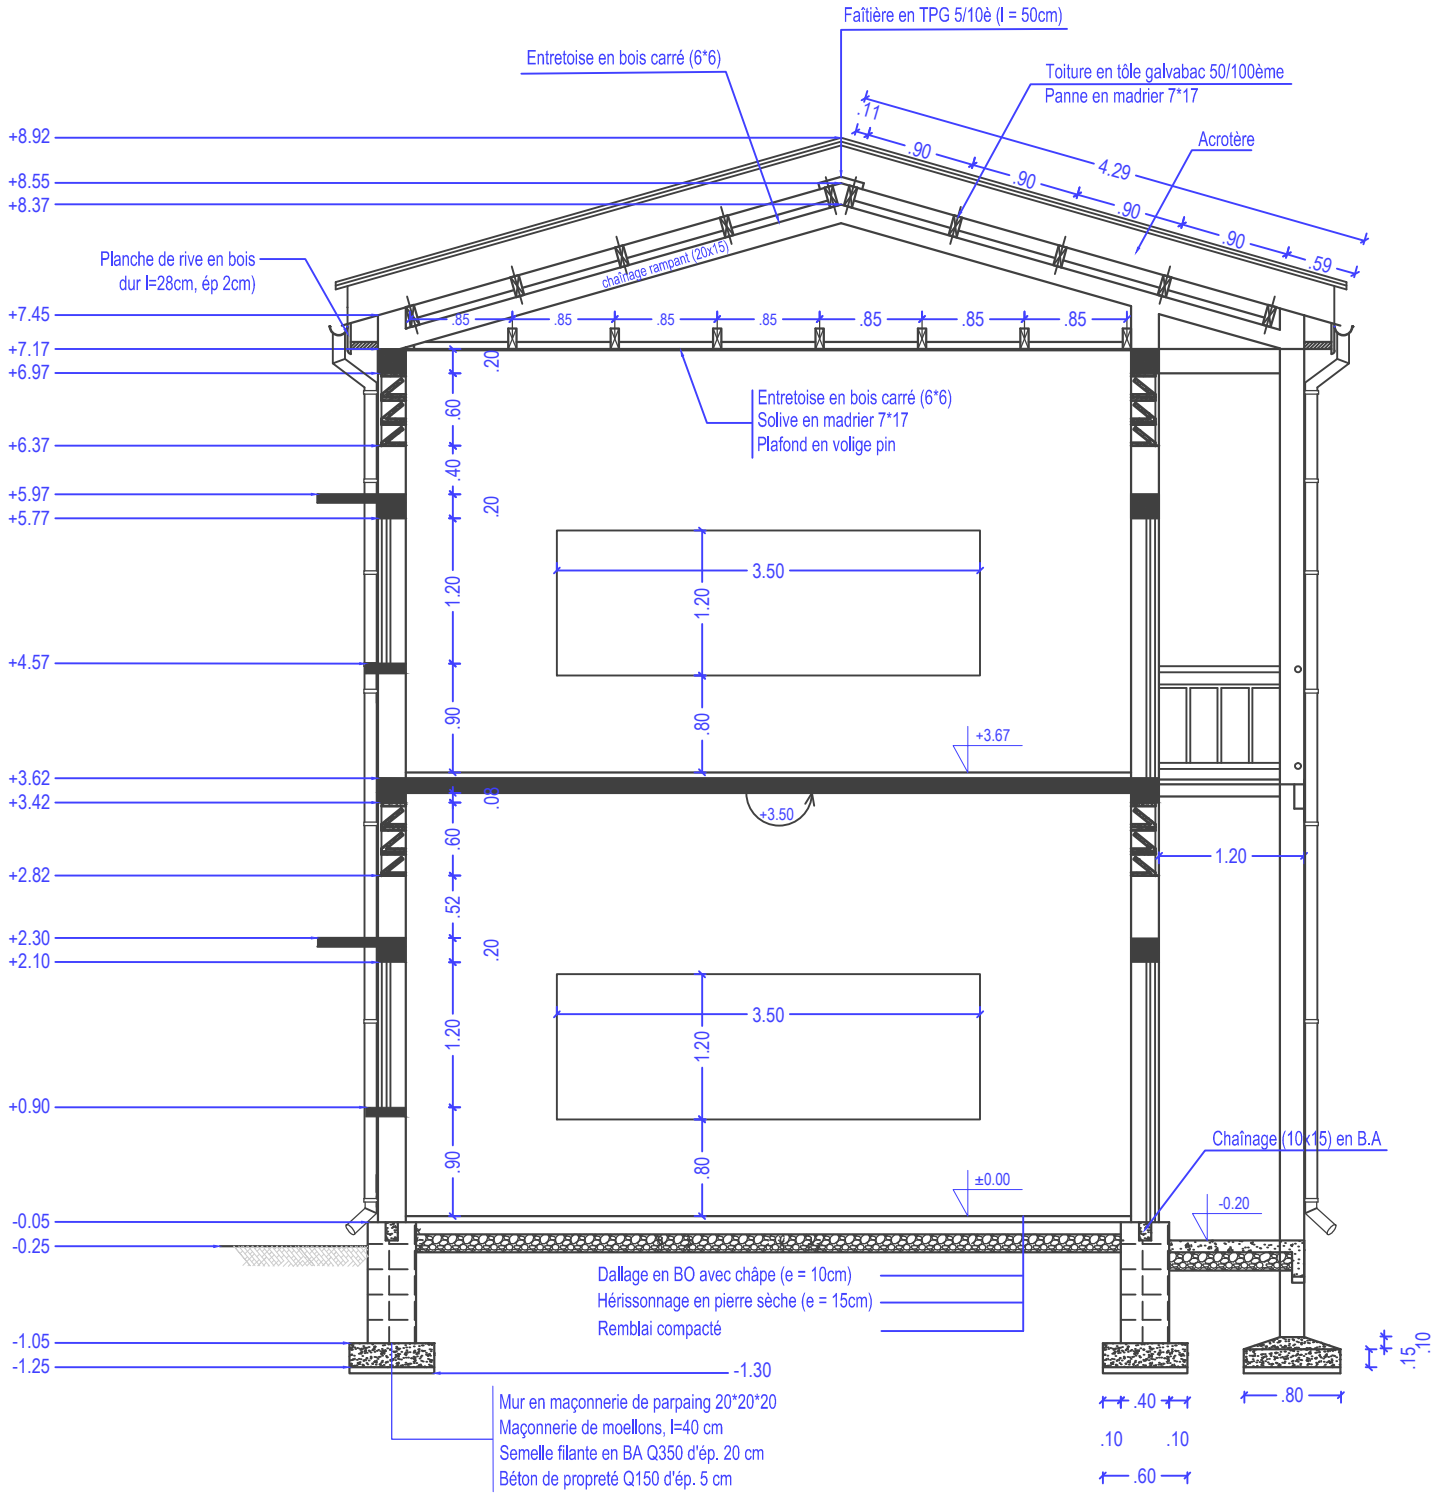
Faîtière en TPG 5/10è (l = 50cm)
Entretoise en bois carré (6*6)
Toiture en tôle galvabac 50/100ème
Panne en madrier 7*17
Acrotère
.11
.90
.90
.90
.90
.59
4.29
+8.92
+8.55
+8.37
Planche de rive en bois
dur l=28cm, ép 2cm)
chaînage rampant (20x15)
+7.45
+7.17
+6.97
+6.37
+5.97
+5.77
+4.57
+3.62
+3.42
+2.82
+2.30
+2.10
+0.90
-0.05
-0.25
-1.05
-1.25
.85
.85
.85
.85
.85
.85
.85
Entretoise en bois carré (6*6)
Solive en madrier 7*17
Plafond en volige pin
.20
.60
.40
.20
1.20
.90
3.50
1.20
.80
+3.67
.03
+3.50
1.20
.60
.52
.20
1.20
.90
3.50
1.20
.80
±0.00
Chaînage (10x15) en B.A
-0.20
Dallage en BO avec châpe (e = 10cm)
Hérissonnage en pierre sèche (e = 15cm)
Remblai compacté
-1.30
Mur en maçonnerie de parpaing 20*20*20
Maçonnerie de moellons, l=40 cm
Semelle filante en BA Q350 d'ép. 20 cm
Béton de propreté Q150 d'ép. 5 cm
.40
.10
.10
.60
.80
.15
.10

COUPE BB